
Perpustakaan perguruan tinggi

Buku pedoman

Edisi kedua

Departemen Pendidikan dan Kebudayaan Rl
Direktorat Jenderal Pendidikan Tinggi
1994

RUANGAN 50 M^2
DAERAH KOLEKSI & PEMBACA : 39.50 M^2 (79%)
DAERAH KERJA STAF : 10.50 M^2 (21%)

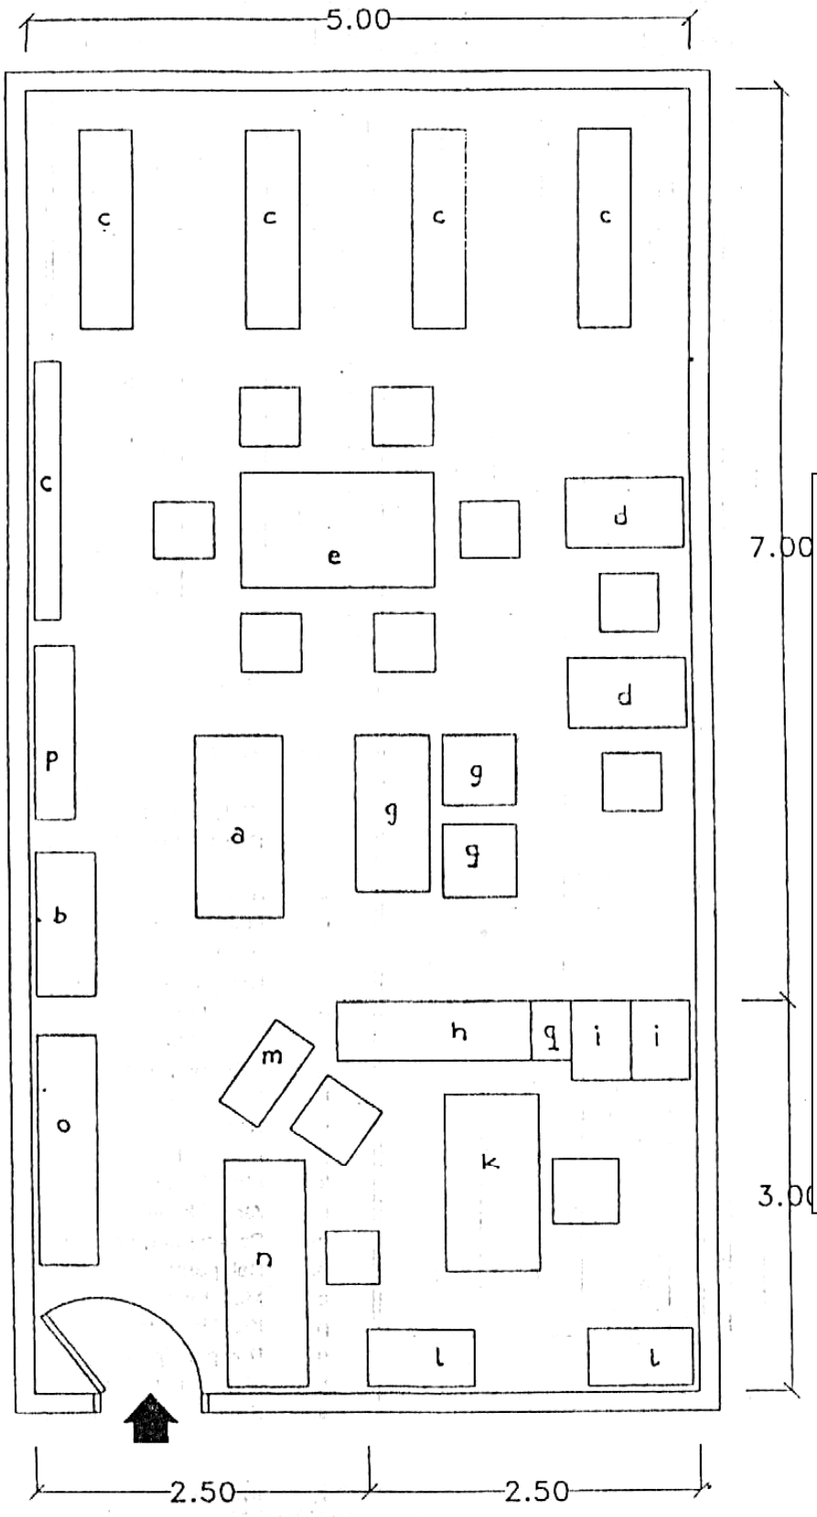


• . KETERANGAN
(RUANGAN: 50 M2)

a. Rak pameran
b. Kabinel katalog
c. Rak buku
d. • Meja **bgca** tunggal
e. Meja **baca**
t. Rak **buku**
fl. Meja hursi lamu
h. Hak buku rendah
*1. Kablnet lHIIng
j. Rak buku
k. Meja + Rural lulia
I. Almari kantor
rn. Mnja ketik beroda
n. Msja psminjaman
o. Rak penitipan barang
p-1 papan pameran / pengurnuman

CONTOH PERPUSTAKAAN
DENGAN LUAS LANTAI 50 M^2

RUANGAN 250 M^2
DAERAH KOLEKSI & PEMBACA : 192 M^2 (77%)
DAERAH KERJA STAF : 58 M^2 (23%)

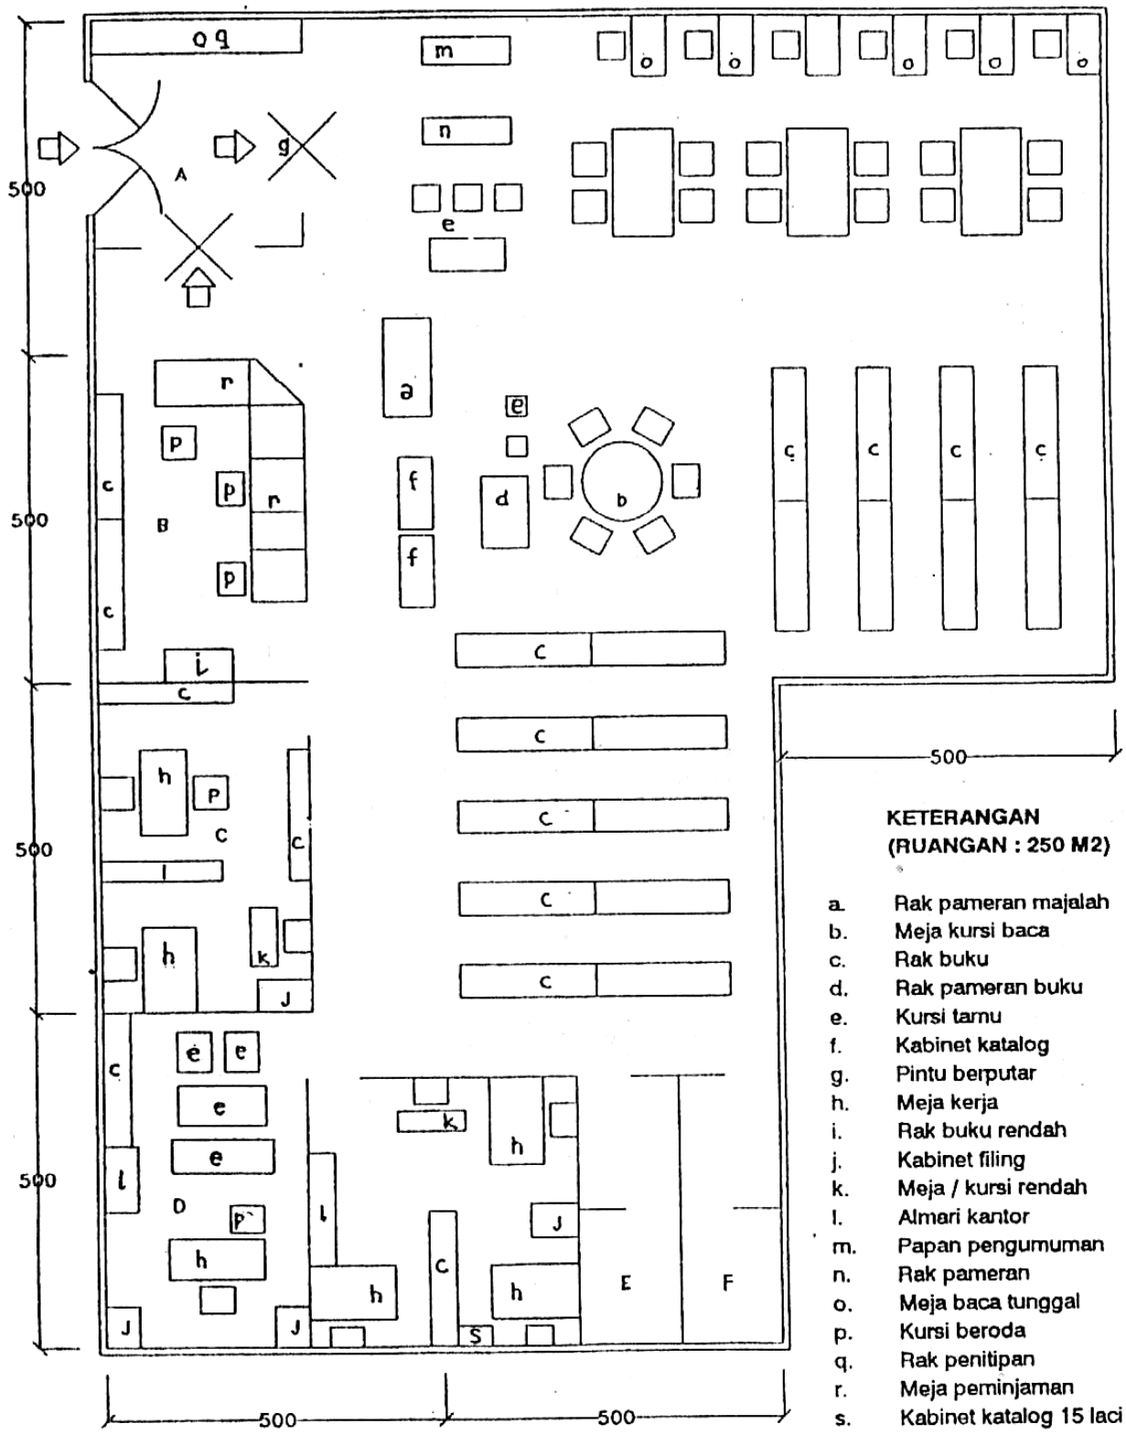


KETERANGAN
(RUANGAN : 250 M2)

a. Rak pameran majalah
b. Meja kursi baca
c. Rak buku
d. Rak pameran buku
e. Kursi tamu
f. Kabinet katalog
g. Pintu berputar
h. Meja kerja
i. Rak buku rendah
j. Kabinet filing
k. Meja / kursi rendah
l. Almari kantor
m. Papan pengumuman
n. Rak pameran
o. Meja baca tunggal
p. Kursi beroda
q. Rak penitipan
r. Meja peminjaman
s. Kabinet katalog 15 laci


A. Peminjaman
B. Administarsi
C. Kepala
D. Pengadaan dan pengolahan
E. W.C. Pria
F. W.C. Wanita

CONTOH PERPUSTAKAAN
DENGAN LUAS LANTAI 250 M^2

RUANGAN 3000 M^2
DAERAH PEMBACA : 2180 M^2 (73%)
DAERAH KERJA : 820 M^2 (27%)

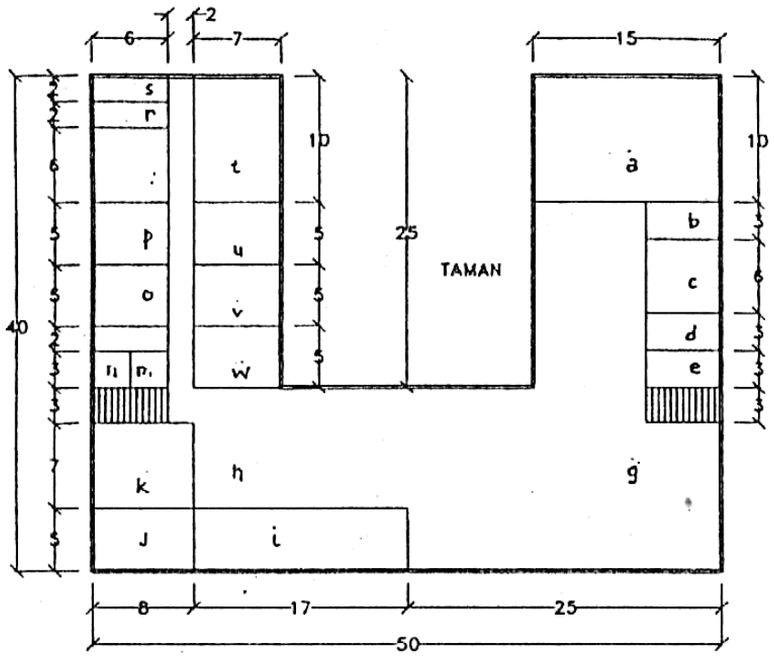

LANTAI BAWAH

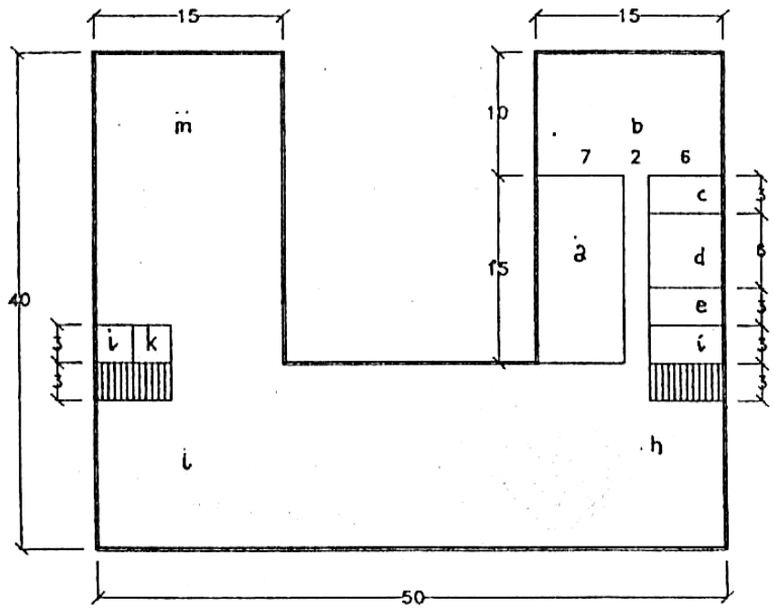

LANTAI ATAS

SKALA 1 : 500

KETERANGAN
(RUANGAN : 3.000 M2)


LANTAI BAWAH

a. Ruang koleksi khusus
b. Gudang alat pandang dengar (AV)
c. Koleksi pandang dengar
d. WC Wanita
e. WC Pria
f. Tangga
g. Ruang referens
h. Peminjaman dan photo copy
i. Lobby
j. Gudang buku baru
k. Pengadaan dan pengolahan
l. Tangga
m. Lift buku
o. Wakil direktur
p. Ketenagaan dan keuangan
q. Dapur
r. WC Wanita
s. WC Pria
t. Penjilidan
u. Perlengkapan
v. Direktur
w. Sekretariat


LANTAI ATAS

a. Ruang diskusi
b. Ruang sidang
c. Gudang ruang sidang
d. Dapur
e. WC Wanita
f. WC Pria
g. Tangga
h. Ruang baca
i. Rak majalah
j. Tangga
k. Lift buku
l. Ruang panel listrik
m. Rak buku


CONTOH PERPUSTAKAAN
DENGAN LUAS LANTAI 250 M^2

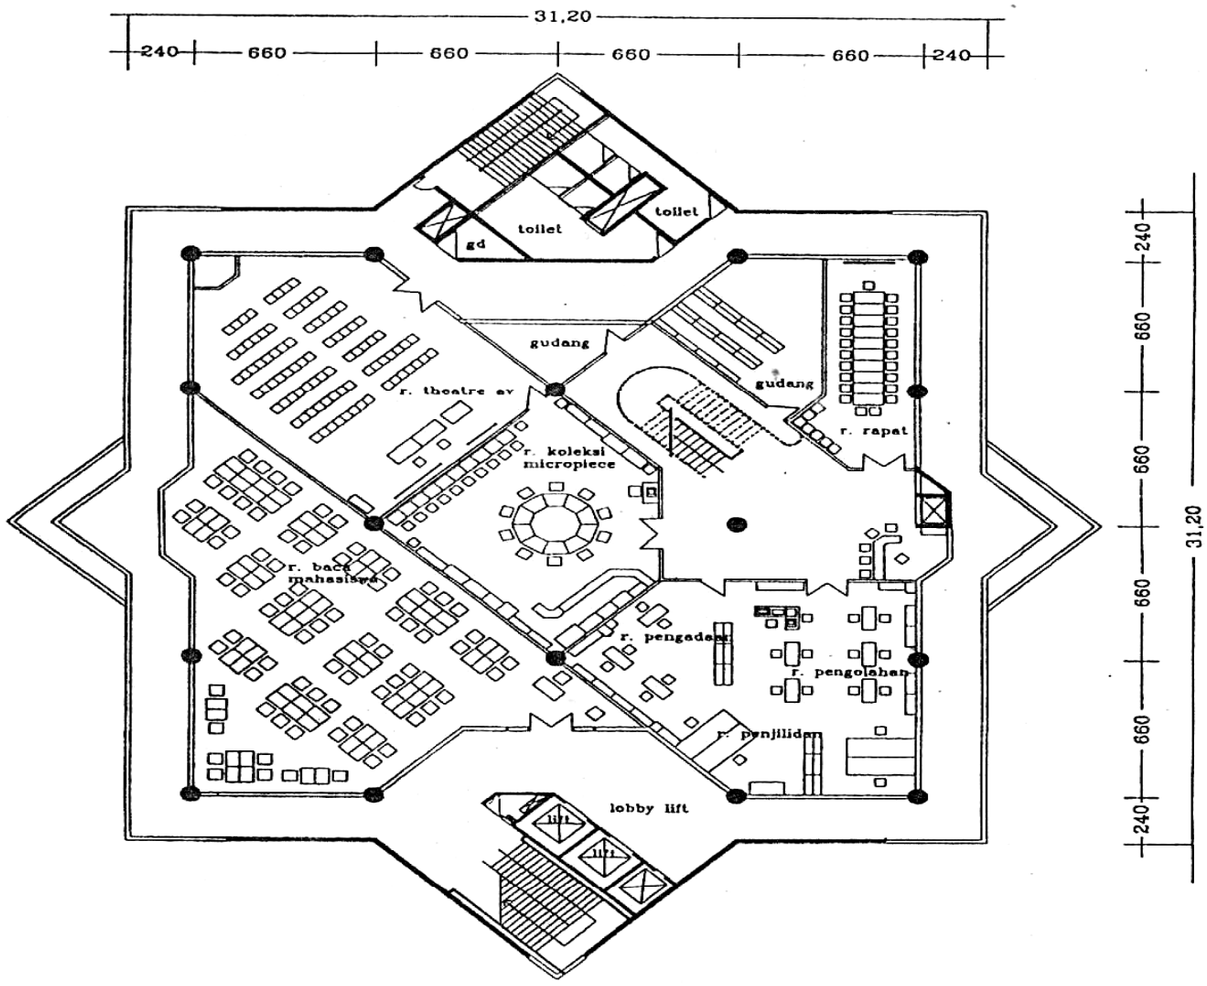


CONTOH LANTAI I (IV) DARI
SALAH SATU PERPUSTAKAAN PERGURUAN TINGGI

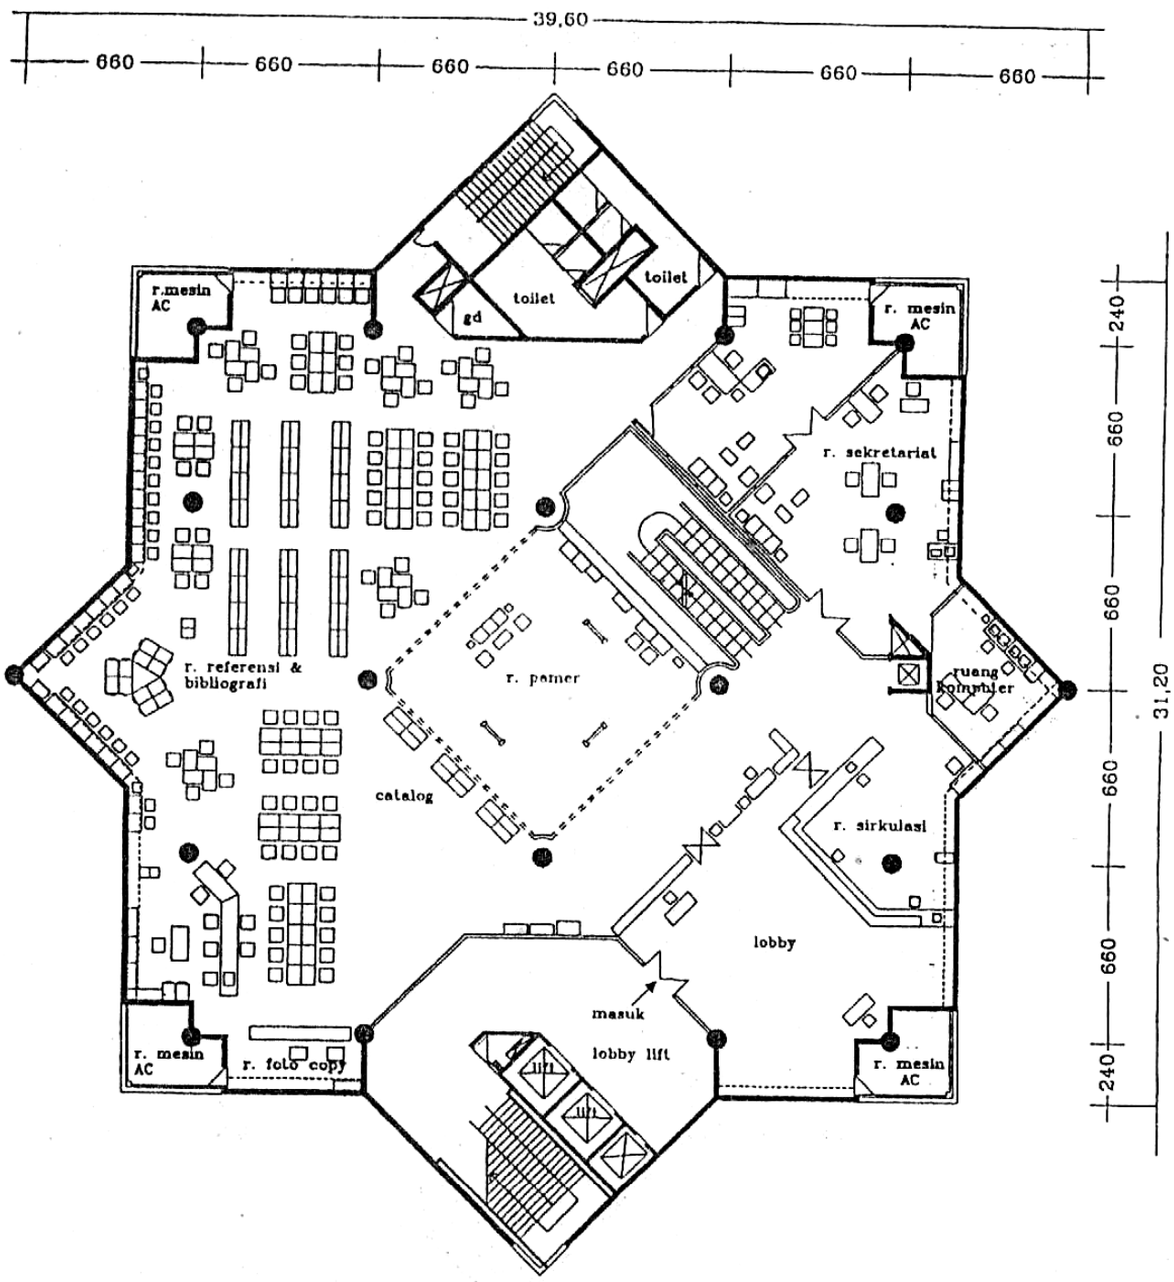

CONTOH LANTAI II (V) DARI
SALAH SATU PERPUSTAKAAN PERGURUAN TINGGI

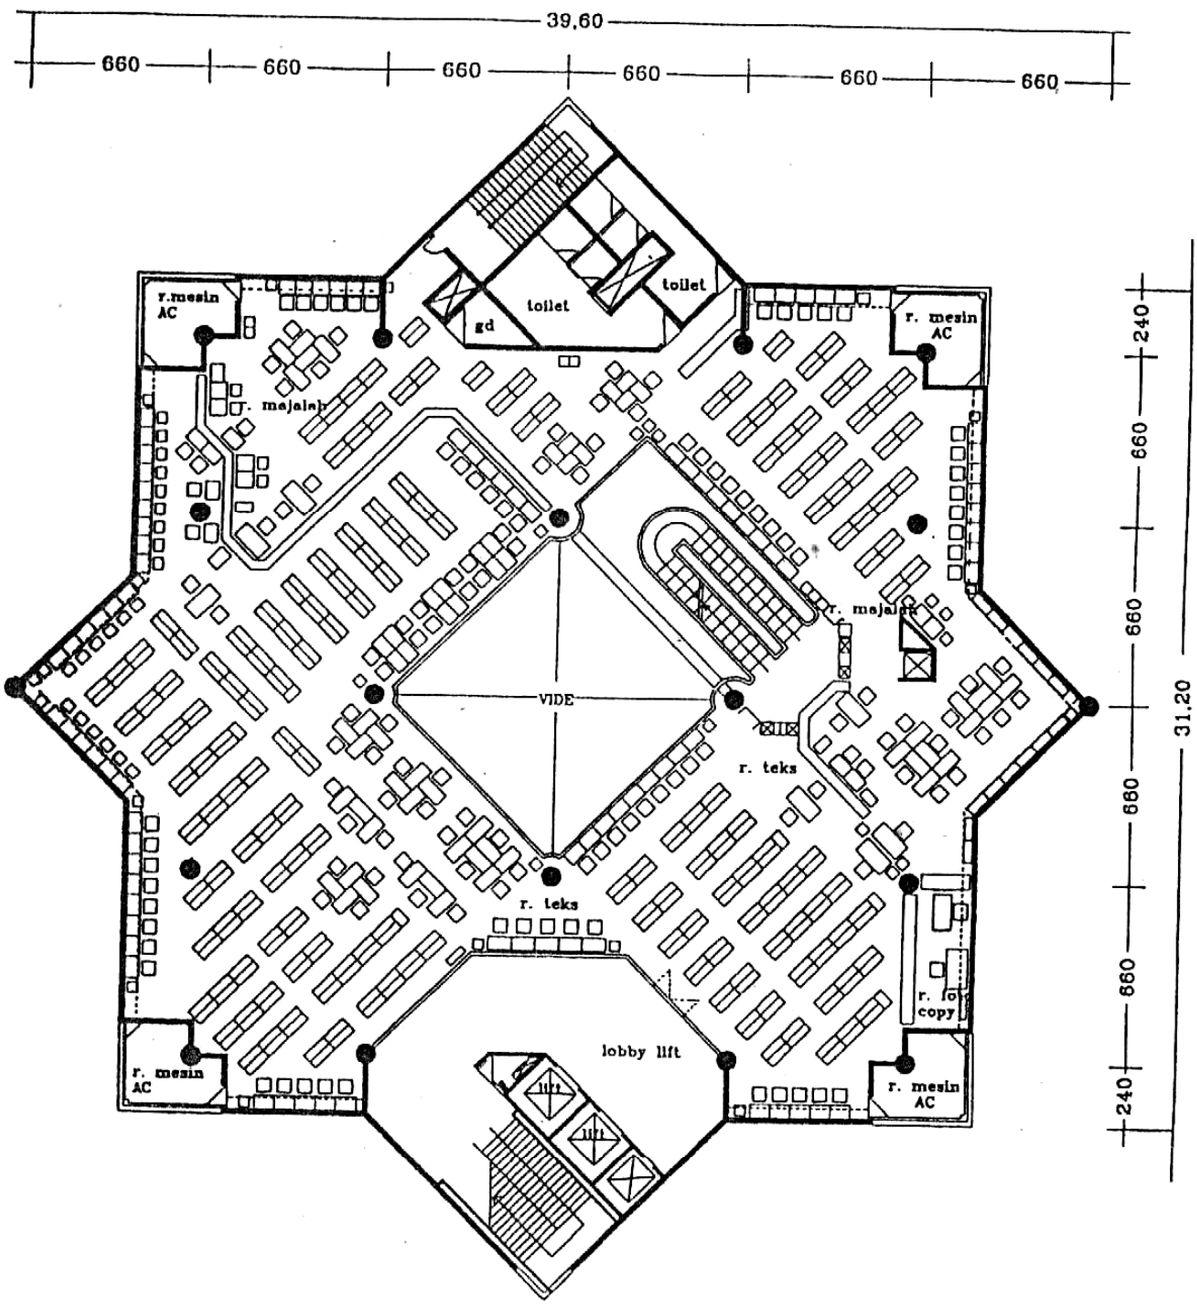

CONTOH LANTAI III (VI) DARI
SALAH SATU PERPUSTAKAAN PERGURUAN TINGGI

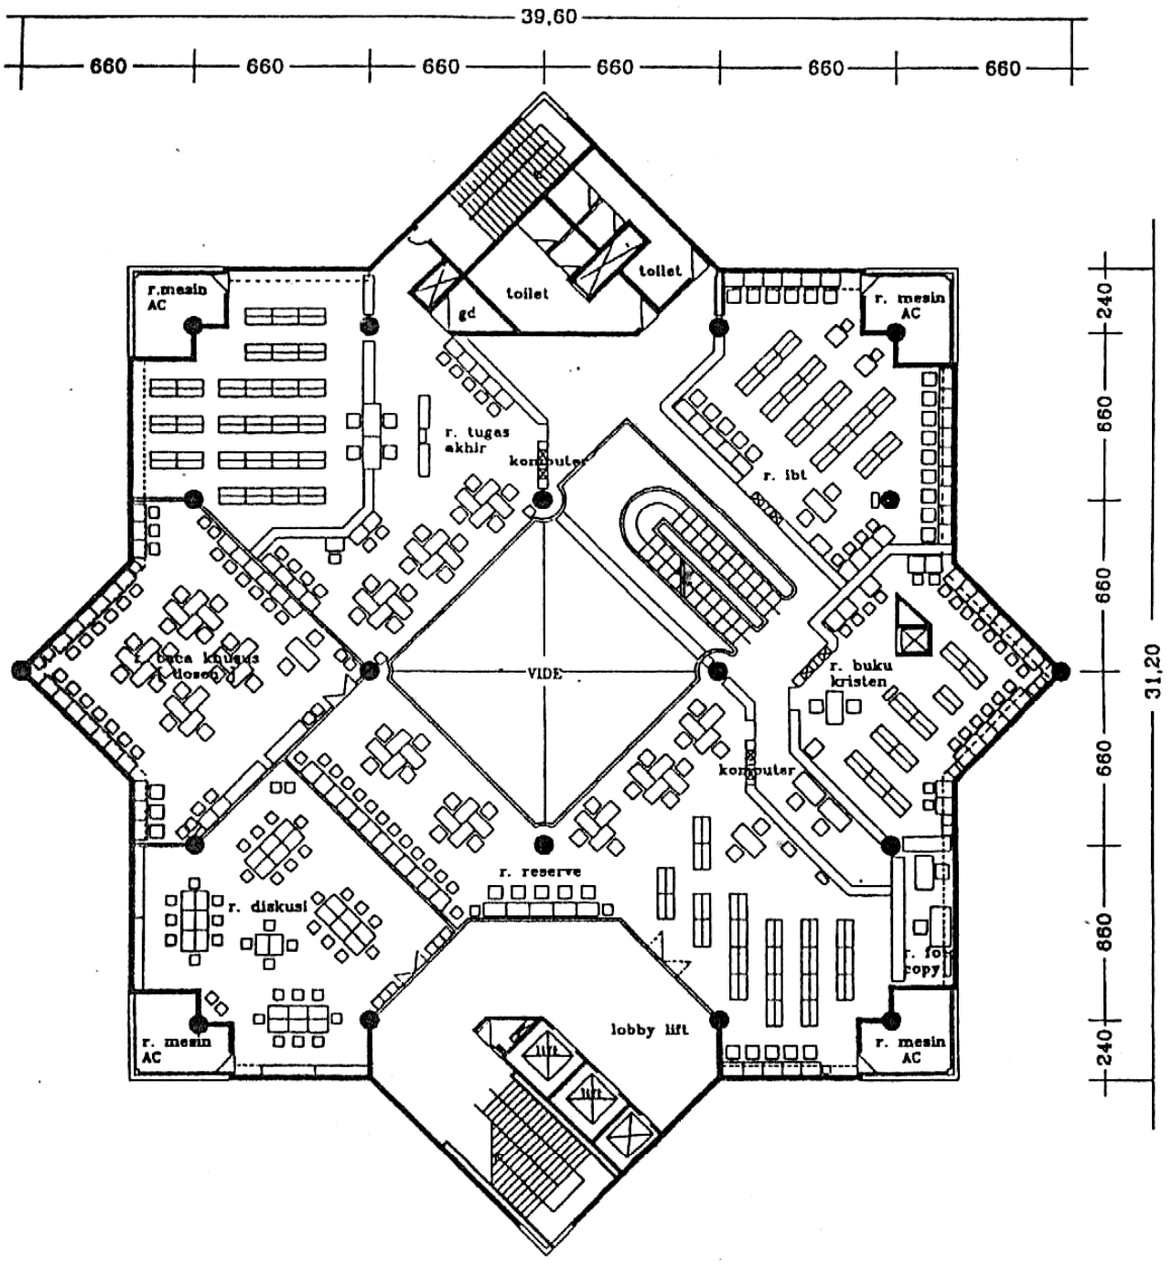

CONTOH LANTAI I (VII) DARI
SALAH SATU PERPUSTAKAAN PERGURUAN TINGGI